

OBJET DE LA DEMANDE (RÉVISION B)

Fermeture d’un porche couvert existant attenant à l’escalier d’entrée (emprise au sol et volumétrie inchangées, ≈ 8 m² de surface de plancher créée), réorganisé en deux volumes : un sas d’entrée (palier ≈ 2.00 × 1.40 m) à la tête de l’escalier existant conservé, fermé par une porte vitrée isolante K1 en aluminium à rupture de pont thermique ($U_w \leq 1.6 \text{ W/m}^2\text{K}$, serrure de sûreté RC2) implantée dans un plan perpendiculaire à la façade, et un vestiaire (≈ 2.00 × 2.50 m) séparé du sas par une cloison légère intérieure. Aucune porte n’est créée en façade : la travée ouverte est fermée par un mur en parpaings de 20 enduit monocouche gratté fin au ton de la façade existante, percé d’une bande vitrée fixe en partie haute (≈ 1000 × 450) et de deux grilles de ventilation du vide sanitaire ; l’ancienne porte côté escalier est murée. La fenêtre à barreaux existante est supprimée (baie maçonnerie). Plancher rehaussé de +0.30 à +1.25 (poutrelles-hourdis sur vide sanitaire ventilé). La toiture existante est conservée sans modification.

Pièce	Désignation	État
DP1	Plan de situation du terrain (extrait IGN / cadastre)	À joindre — extrait cadastral
DP2	Plan de masse coté dans les trois dimensions	Planche 2 — cotes aux limites à vérifier
DP3	Plan en coupe du terrain et de la construction	Planche 3
DP4	Plan des façades et des toitures (état existant / projeté)	Planche 4 — aucune porte en façade (entrée K1 en retour)
DP5	Plan des toitures	SANS OBJET — toiture existante conservée sans modification (voir note ci-dessous)
DP6	Document graphique d’insertion (photomontage)	À joindre — montage sur photo n°1
DP7	Photographie situant le terrain dans l’environnement proche	À joindre — photo n°1 du dossier
DP8	Photographie situant le terrain dans le paysage lointain	À joindre — photo depuis la voie

NOTE DP5 — TOITURE

La toiture du porche est existante et strictement conservée : aucune modification de pente, de matériau ni d’égout. Le mur neuf est arasé sous la sous-face existante avec joint compressible et mastic (aucune liaison rigide à la charpente). En conséquence la pièce DP5 est sans objet ; la volumétrie est lisible sur les planches DP3 et DP4.

RENSEIGNEMENTS À COMPLÉTER AU DÉPÔT

- Demandeur : nom, adresse, coordonnées [à compléter]
- Références cadastrales de la parcelle [à compléter]
- Surface de plancher créée : ≈ 8 m² (5 à 20 m² → DP ; à confirmer après relevé)
- Zone PLU et périmètre ABF : réponse écrite du Service Urbanisme à joindre
- Teinte d’enduit : échantillon au ton de la façade existante — référence fabricant à indiquer (l’ABF peut imposer la teinte)
- Contrôle des cotes sur place avant dépôt (relevé laser) — aucune fabrication sur cotes nominales
- Dépôt : guichet numérique de la Ville d’Orange ou 2 à 4 exemplaires papier

LÉGENDE



- Construction existante conservée
- Projet : travée fermée (mur en parpaings de 20, enduit monocouche gratté fin) ; baies murées
- Porte projetée avec sens d'ouverture (K1 vitrée / V)
- Bande vitrée fixe projetée (mur est, partie haute)
- Limite de propriété (schématique)

COTES DANS LES TROIS DIMENSIONS

- Emprise du projet : ≈ 2.00 × 4.00 m (intérieur) — inchangée, sous toiture existante ; sas ≈ 2.00 × 1.40 m + vestiaire ≈ 2.00 × 2.50 m.
- Niveau du plancher projeté : +1.25 (TN ±0.00) — sas et vestiaire au même niveau.
- Hauteur : aucune modification — mur neuf arasé sous la toiture existante (+3.60 env.).
- Accès : escalier existant conservé, puis porte vitrée K1 à la tête de l'escalier — aucune porte créée en façade.
- Réseaux : aucun raccordement nouveau ; eaux pluviales inchangées.


ORGANISATION INTÉRIEURE PROJETÉE

schéma ≈ 1:50 — cotes nominales ; relevé sur site obligatoire avant exécution

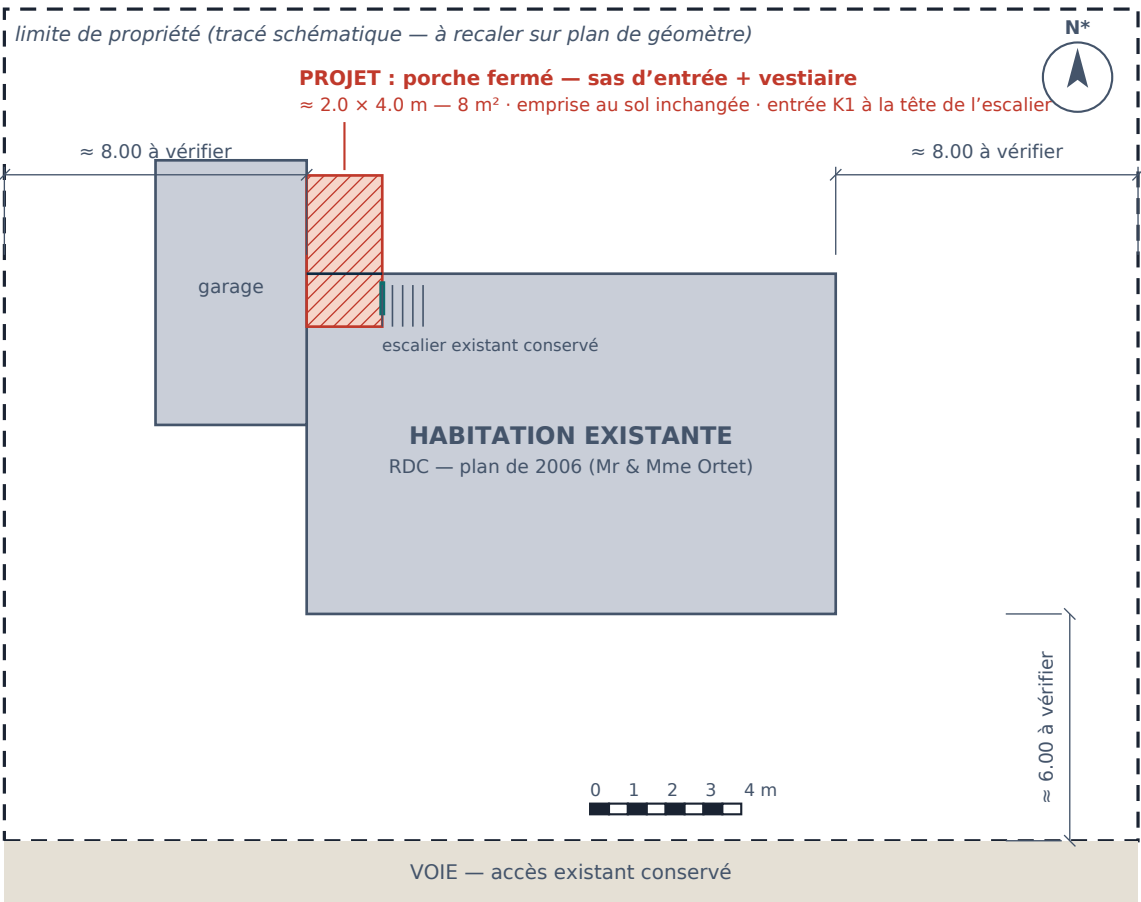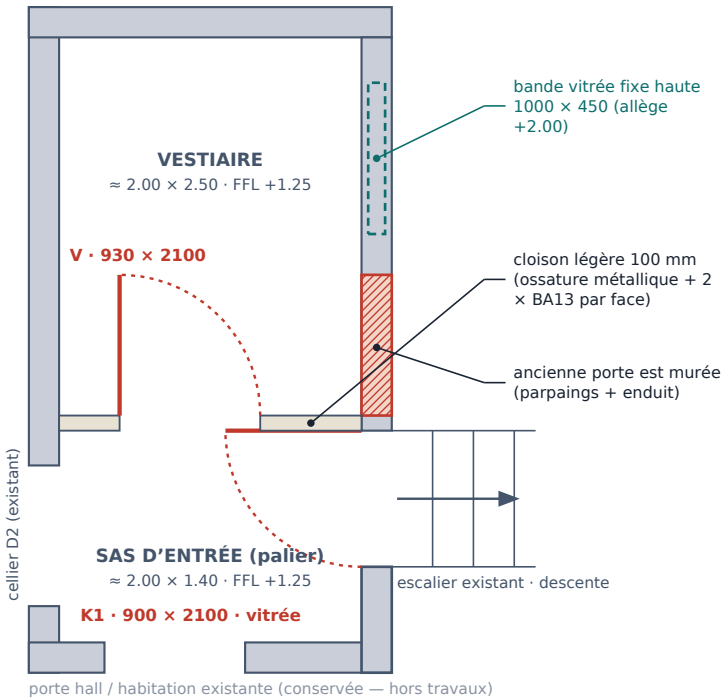

NOTA : distances aux limites séparatives indicatives — contrôle sur place avant dépôt.

PLAN DE MASSE · ÉCHELLE 1:200 @ A3

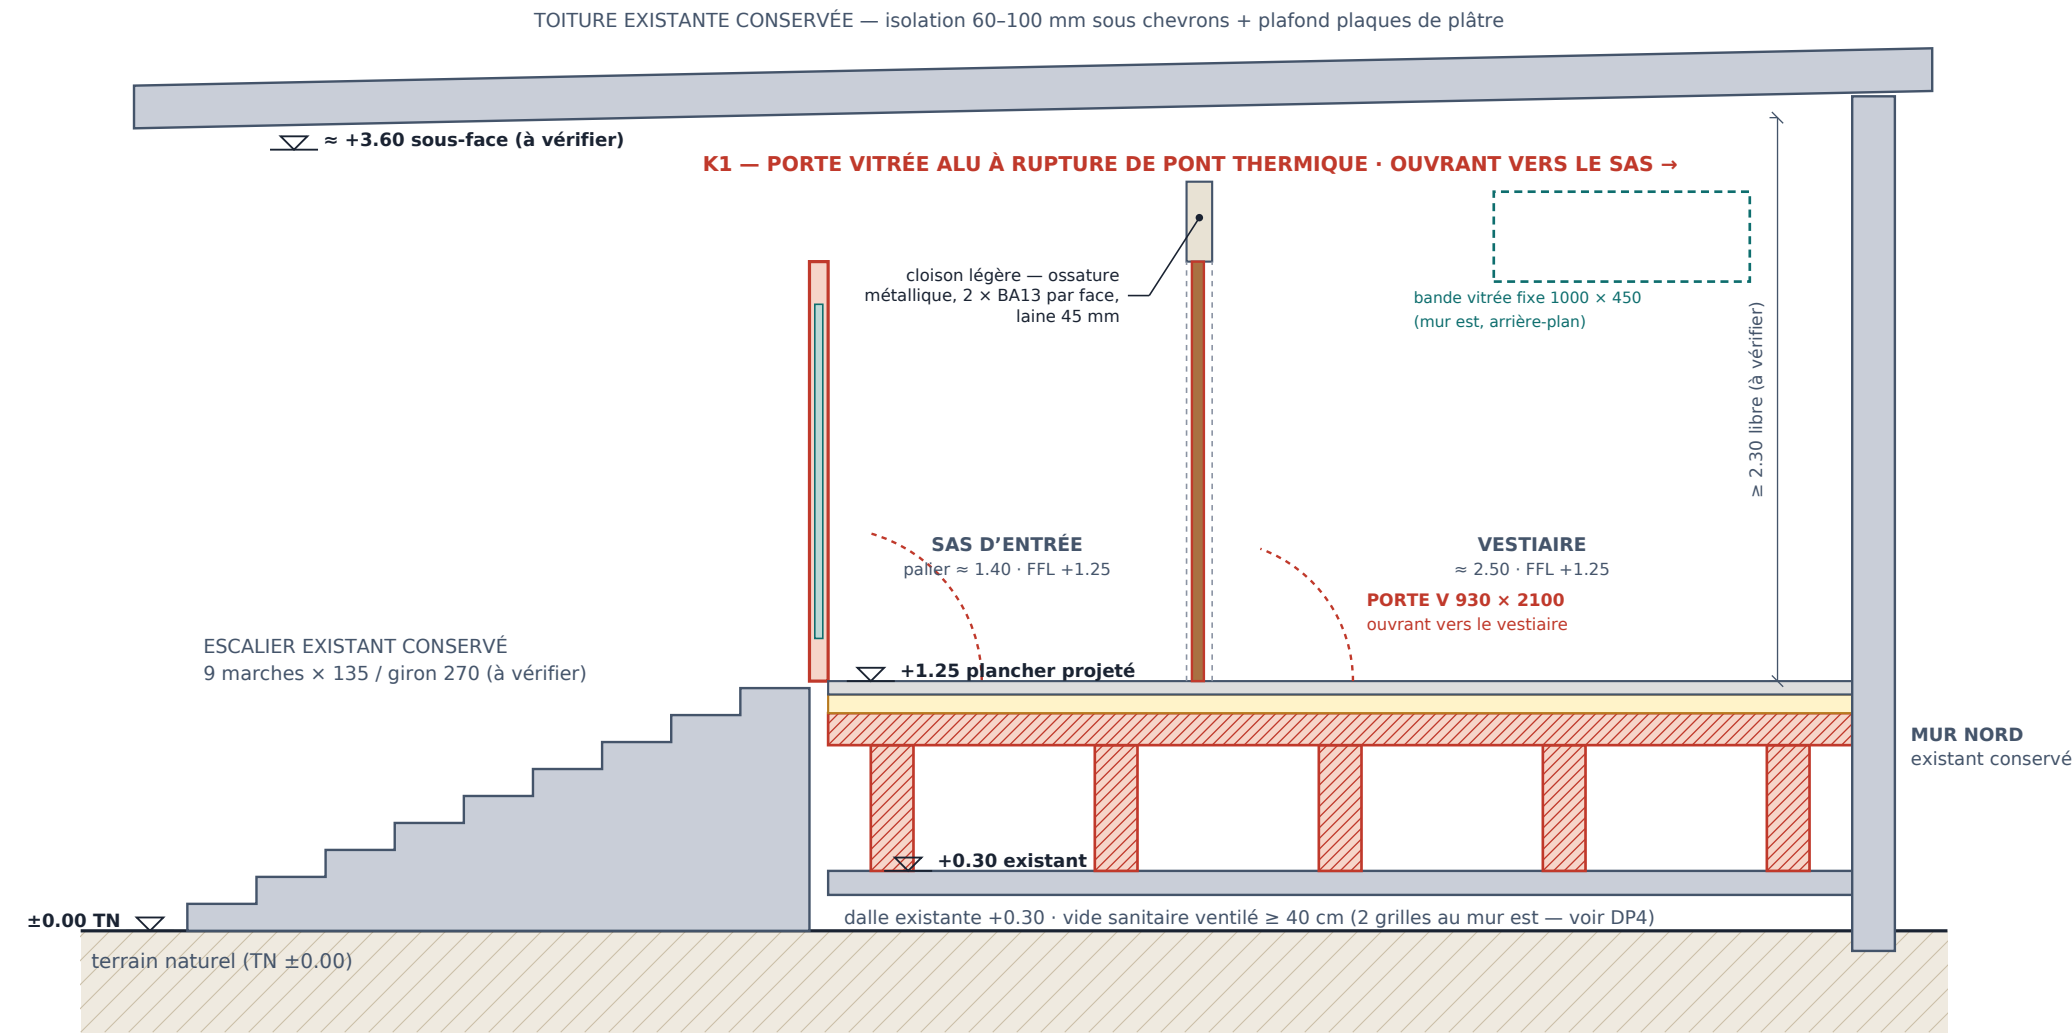

COUPE DÉVELOPPÉE SUR L'ACCÈS (ESCALIER → K1 → SAS → VESTIAIRE) · ÉCHELLE ≈ 1:35 @ A3


NOTICE TECHNIQUE (COUPE)

- Plancher rehaussé de +0.30 à +1.25 : poutrelles-hourdis sur murets, vide sanitaire ventilé (2 grilles au mur est).
- K1 900 × 2100 : porte vitrée en aluminium à rupture de pont thermique, $U_w \leq 1.6 \text{ W/m}^2\text{K}$, serrure de sûreté RC2, ferme-porte ; seuil $\leq 20 \text{ mm}$.
- Sas d'entrée ≈ 2.00 × 1.40 m : volume tampon thermique et de sûreté entre l'escalier et l'habitation.
- Cloison sas/vestiaire : ossature métallique + 2 × BA13 par face, laine minérale 45 mm ; porte V 930 × 2100 ouvrant vers le vestiaire.
- Mur est neuf en parpaings de 20 sur semelle filante 50 × 25 (hors gel ≥ 60 cm), chaînage 4 HA10 — hors plan de coupe, voir DP4 ; ancienne porte côté escalier murée.
- Bande vitrée fixe 1000 × 450 en partie haute du mur est (allège à +2.00 du plancher) — éclairement naturel du vestiaire.
- Isolation : murs et plancher $R \geq 3.0$, plafond $R \geq 4.5 \text{ m}^2\text{K/W}$ (RT existant, élément par élément).
- Joint compressible + mastic en tête du mur neuf — aucune liaison rigide à la charpente ; toiture et terrain naturel inchangés.


SENS D'OUVERTURE — JUSTIFICATION (SÉCURITÉ)

K1 s'ouvre vers l'intérieur du sas, jamais au-dessus de l'escalier : un vantail ouvrant sur le vide pousserait l'utilisateur vers la première marche et heurterait toute personne montant l'escalier (risque de chute). Charnières côté nord : le vantail ouvert se rabat contre le mur nord du palier sans gêner la porte du hall. Ferme-porte contre les coups de vent.

V s'ouvre vers le vestiaire (palier étroit : 1.40 m), charnières à l'ouest : le vantail se rabat contre le flanc du meuble W1 et laisse libre l'axe d'entrée porte → miroir. Les deux vantaux ouverts restent dans des volumes distincts — aucun conflit. La porte du hall existante est conservée telle quelle (hors travaux).

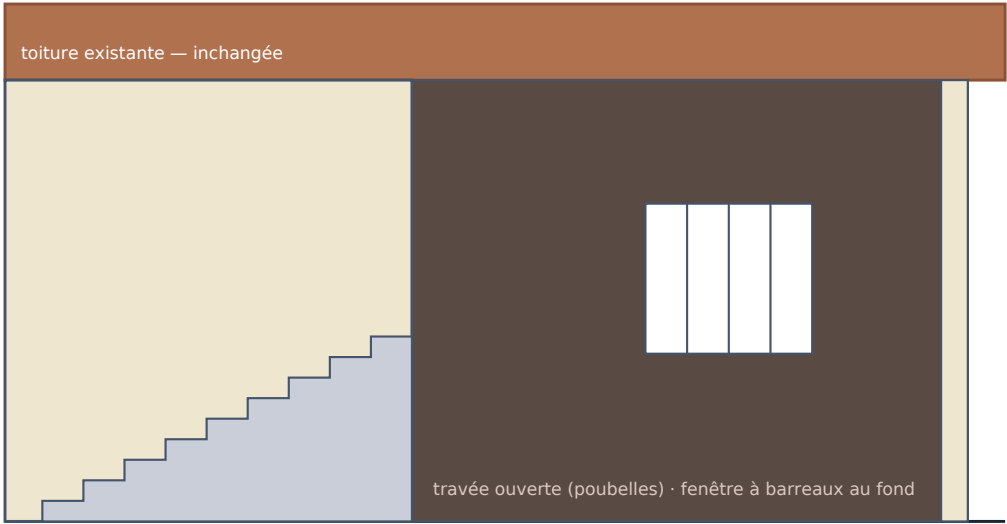

ÉTAT EXISTANT · façade sur voie · ≈ 1:60

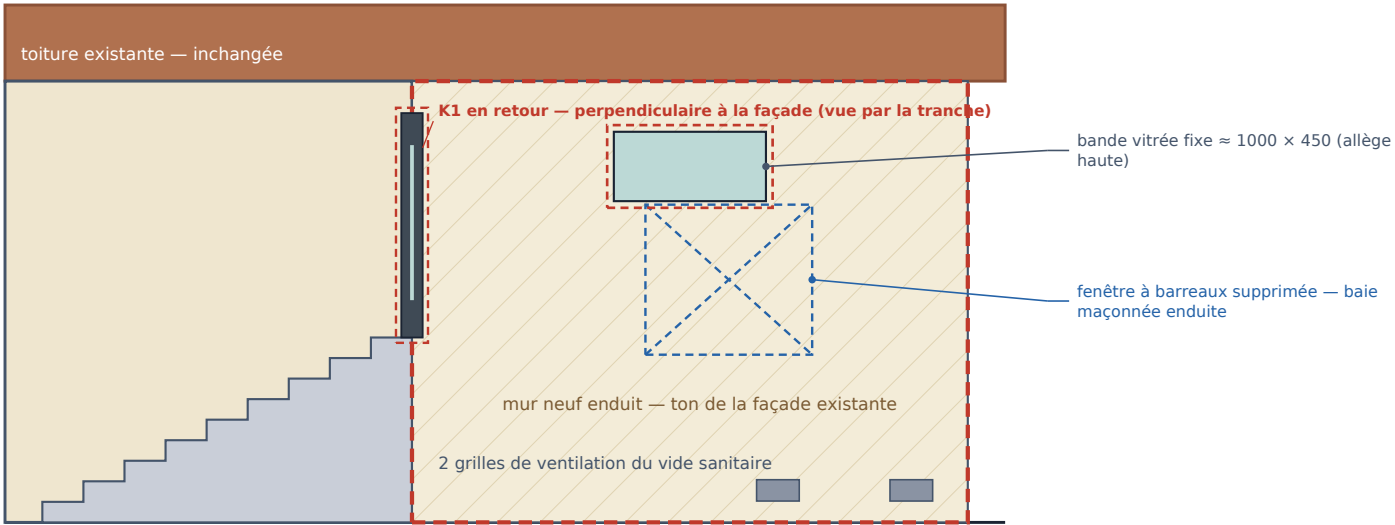

ÉTAT PROJETÉ · façade sur voie · ≈ 1:60

MODIFICATIONS DÉCLARÉES (ÉTAT PROJETÉ)

- Fermeture de la travée ouverte par un mur en parpaings de 20, enduit monocouche gratté fin au ton de la façade existante — AUCUNE porte créée en façade.
- L’accès se fait par l’escalier existant conservé puis par la porte vitrée K1 (900 × 2100, aluminium à rupture de pont thermique, $U_w \leq 1.6$) implantée à la tête de l’escalier, dans un plan perpendiculaire à la façade — visible uniquement par la tranche sur l’état projeté.
- Bande vitrée fixe en partie haute (≈ 1000 × 450, vitrage feuilleté, allège à +2.00 du plancher) — éclairement naturel du vestiaire.
- Suppression de la fenêtre à barreaux existante — baie maçonnerie et enduite au même ton (invisible à l’état fini) ; ancienne porte côté escalier murée.
- Deux grilles de ventilation en partie basse (vide sanitaire).
- Toiture, escalier, accès et niveaux du terrain : inchangés.

INSERTION PAYSAGÈRE

Le projet reprend strictement la volumétrie existante (aucune surélévation, aucune emprise nouvelle) et ne crée aucune menuiserie en façade hormis la bande vitrée haute : la porte vitrée K1, en retour perpendiculaire, n’est pas perceptible depuis la voie. Enduit au ton de la façade existante, menuiseries sobres de teinte foncée. Dans le périmètre des abords des Monuments Historiques, la teinte définitive sera soumise à l’avis de l’Architecte des Bâtiments de France ; un échantillon pourra être fourni.