

Ek Karar: K1 — Rüzgarlık Kapısı

Merdiven başı sahanlığını kapatan camlı, kilitli dış kapı — güvenlik + ısı tamponu

EK · K1 RÜZGARLIK KAPISI (ESKİ KOD D3)

Orange (84100) · Vaucluse · Fransa

Temmuz 2026 · Rev B · ana paketin ekidir

Rev B sirkülasyonu: merdivenden çıkılır → K1 → sahanlık → solda mevcut ev kapısı, sağda V kapısı → vestiyer. Önceki tasarlarda D3 koduyla geçen bu kapı, Rev B'de resmi adını aldı: K1 (rüzgarlık/tampon kapısı). Eski doğu (merdiven tarafı) vestiyer kapısı İPTAL — örülür.


NEDEN

- Güvenlik: sokaktan merdivenle doğrudan eve ulaşım kapanır; K1 kilitlidir (RC2). Camlı kanat sayesinde gelen kişi içeriden görülür.
- Isı: sahanlık bir ara tampon (sas) olur. Ev kapısı veya V açıldığında sıcak hava doğrudan dışarı kaçmaz.

NE YAPILACAK

- Camlı, ısı yalıtımlı (thermal-break) alüminyum TEK kanat dış kapı — merdiven başı, sahanlığın doğu kenarı.
- Hedef ısı geçirgenliği: $U_w \leq 1.6 \text{ W/m}^2\text{K}$ · eşik $\leq 20 \text{ mm}$ (s.2).
- RC2 sınıfı kilit takımı + kendinden kapanan menteşe.
- Kanat $\approx 900 \times 2100 \text{ mm}$ (net geçiş biraz daha dar). Kesin ölçü YERİNDE alınır — imalat öncesi yerinde ölçü zorunludur.

NEREDE — KROKİ (ÖLÇEKSİZ)

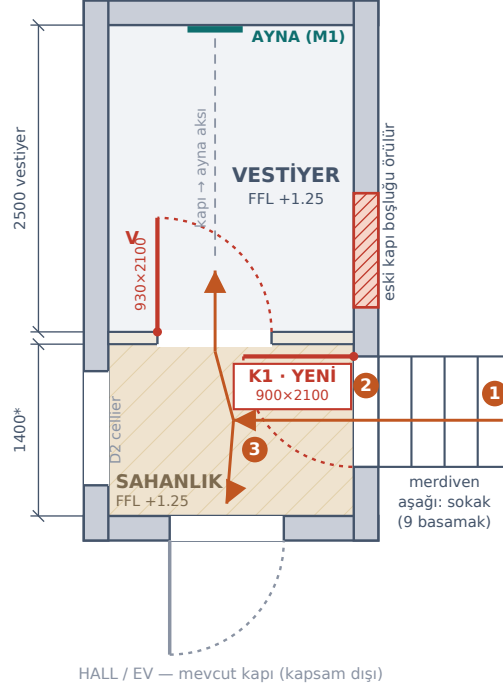

- Sirkülasyon: ① merdiven → ② K1 → ③ sahanlık — solda (güney) mevcut ev kapısı, sağda (kuzey) V → vestiyer.
- K1 sahanlığa, V vestiyere İÇE açılır (kırmızı); giren kişi aynayı (M1) tam karşısında görür.
- Gri: mevcut / kapsam dışı. Eski doğu kapısı örülür (taralı). *Sahanlık derinliği 1400 mm VARSAYIM; iç genişlik 2000.

BÜTÇE — MERTEBE TAHMİNİ

900 - 1.600 €

malzeme + montaj

Kesin fiyat teklifle netleşir. İhale formunda OPSİYON K1 (eski kod D3) ayrı satır olarak fiyatlanır; ana paket toplamına dahil değildir.

YÖN KURALI — K1 SAHANLIĞA İÇE AÇILIR

Merdiven üzerine DIŞA açılan kapı, açan kişiyi merdiven boşluğuna iter ve kanat aşağıdan çıkana çarpar — düşme riski. K1 bu yüzden SAHANLIĞA İÇE açılır; menteşe KUZEY kasadadır (açık kanat kuzey duvara yaslanır, geçişi kapatmaz), kendinden kapanan menteşe rüzgârda çarpmayı keser. V ise dar sahanlığa değil VESTİYERE açılır — iki kanat farklı hacimlerde kalır, çarpışma senaryosu yoktur.

İZİN NOTU — CEPHE DEĞİŞİKLİĞİ

K1 dışarıdan görünür; cephe görünümü değişir. Bu yüzden belediyeye Déclaration Préalable ek/değişiklik bildirimi verilir; önce/sonra cephe çizimi dosyaya eklenir. Onay gelmeden kapı sipariş edilmez ve takılmaz.

ANA PAKETTE İLGİLİ YERLER (REV B)

İmalat çizimleri S-01 Yerleşim Planı (Rev B) · İhale Dosyası — OPSİYON K1 satırı (V kapısı ihale dışıdır) · Eşik sayfası — bu ekin 2. sayfası.

SIRADA: ① sahanlığı ve son basamağı ölçün (derinlik 1400 varsayımdır) ② K1'i DP dosyasına ekletin (değişiklik bildirimi)

③ onay + itiraz süresi geçtikten sonra kapıyı OPSİYON K1 (eski kod D3) olarak sipariş edin.

Eşik Sayfası (K1 + V)

K1 dış eşiği: alçak, sızdırmaz, suyu atar · V iç geçişi: aynı kot, eşiksiz hedef


EK · K1 RÜZGARLIK KAPISI (ESKİ KOD D3)

Orange (84100) · Vaucluse · Fransa

Temmuz 2026 · Rev B · ana paketin ekidir

Kesit K1 (rüzgarlık kapısı) eşiği içindir: takılmadan geçilen alçak eşik, içeride kuru zemin, dışarıda suyu atan denizlik. V bir iç kapıdır: sahanlık ve vestiyer aynı kota (+1.25) yapıldığı için hedef EŞİKSİZ geçiştir — alttaki kurallara bakın.

K1 EŞİĞİ — KESİT ŞEMASI (ÖLÇEKSİZ, ORANLI)

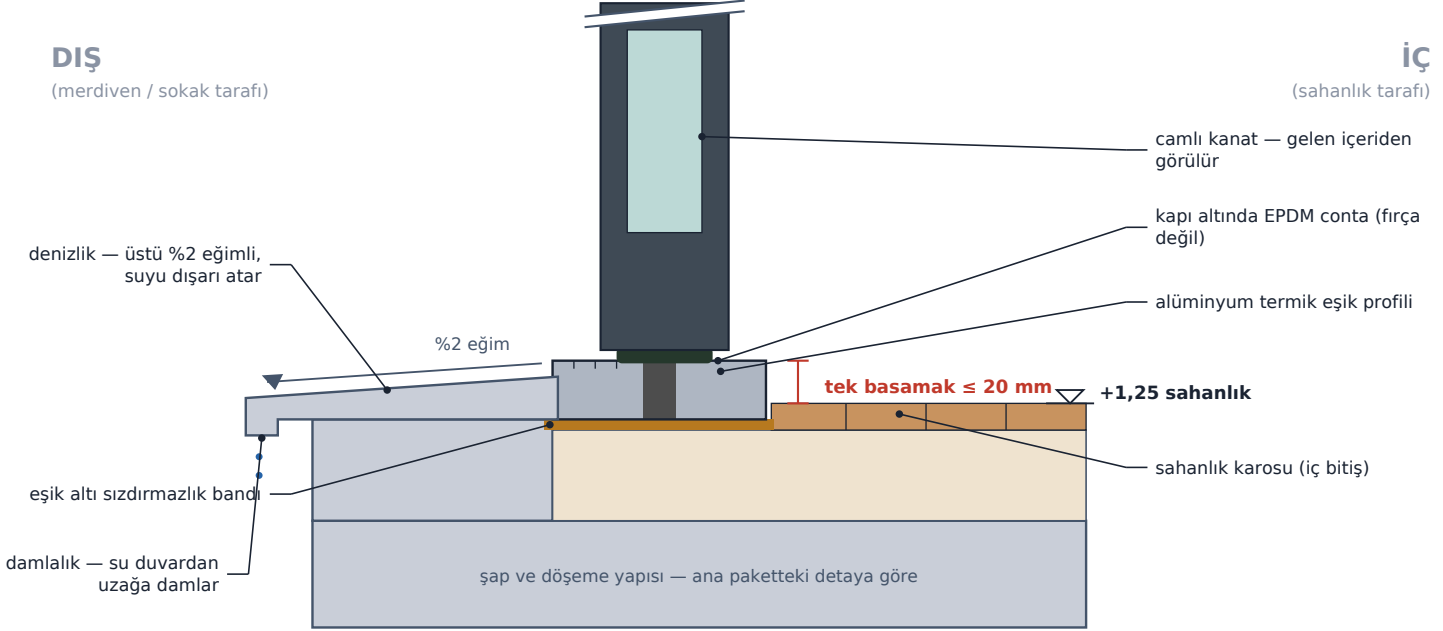

Şema ölçeksizdir; oranlar yaklaşıktır. İmalat öncesi yerinde ölçü zorunludur.

KURALLAR

- K1 önünde tek basamak en fazla 20 mm: daha yüksek eşik ayağa takılır ve erişilebilirliği bozar.
- Eşik altına sızdırmazlık bandı serilir; profil şapa değil, bandın üzerine oturur. Kapı altında fırça değil EPDM conta: hava ve suyu keser.
- Dış denizlik suyu dışarı atar: üstü %2 eğimlidir, damlalık kenarı duvar yüzünden dışarı taşar.
- V iç kapıdır: sahanlık ve vestiyer döşemeleri AYNI kota (+1.25) döküldüğü için eşik konmaz — hedef eşiksiz geçiştir; kapı altında yalnız kanat boşluğu kalır. Yerinde kot farkı çıkarsa ≤ 20 mm kuralı yine geçerlidir.
- Kotlar ve eşik ilişkisi yerinde ölçüyle kesinleşir — data/dimensions.json içindeki değerler verified:false durumundadır.

İKİ KAPI BİR BAKIŞTA

	K1 — rüzgarlık kapısı (eski kod D3)	V — vestiyer kapısı
Konum	Sahanlığın doğu kenarı, merdiven başı	Sahanlık kuzey duvarı (hafif bölme)
Nereye açılır	Sahanlığa, içe — menteşe kuzey	Vestiyere, içe — menteşe batı
Eşik	Bu sayfadaki detay — ≤ 20 mm	Eşiksiz — iki taraf aynı kot (+1.25) hedefi
Isı hedefi	$U_w \leq 1.6$ W/m ² K	$U_d \leq 1.4$ W/m ² K (iç kapı)
Kapsam	OPSİYON K1 — DP değişikliği onayı sonrası	Yerinde tedarik — ihale kapsamı dışı

Bu ek, ana paketteki çizim ve kuralların yerine geçmez; onlarla birlikte okunur.