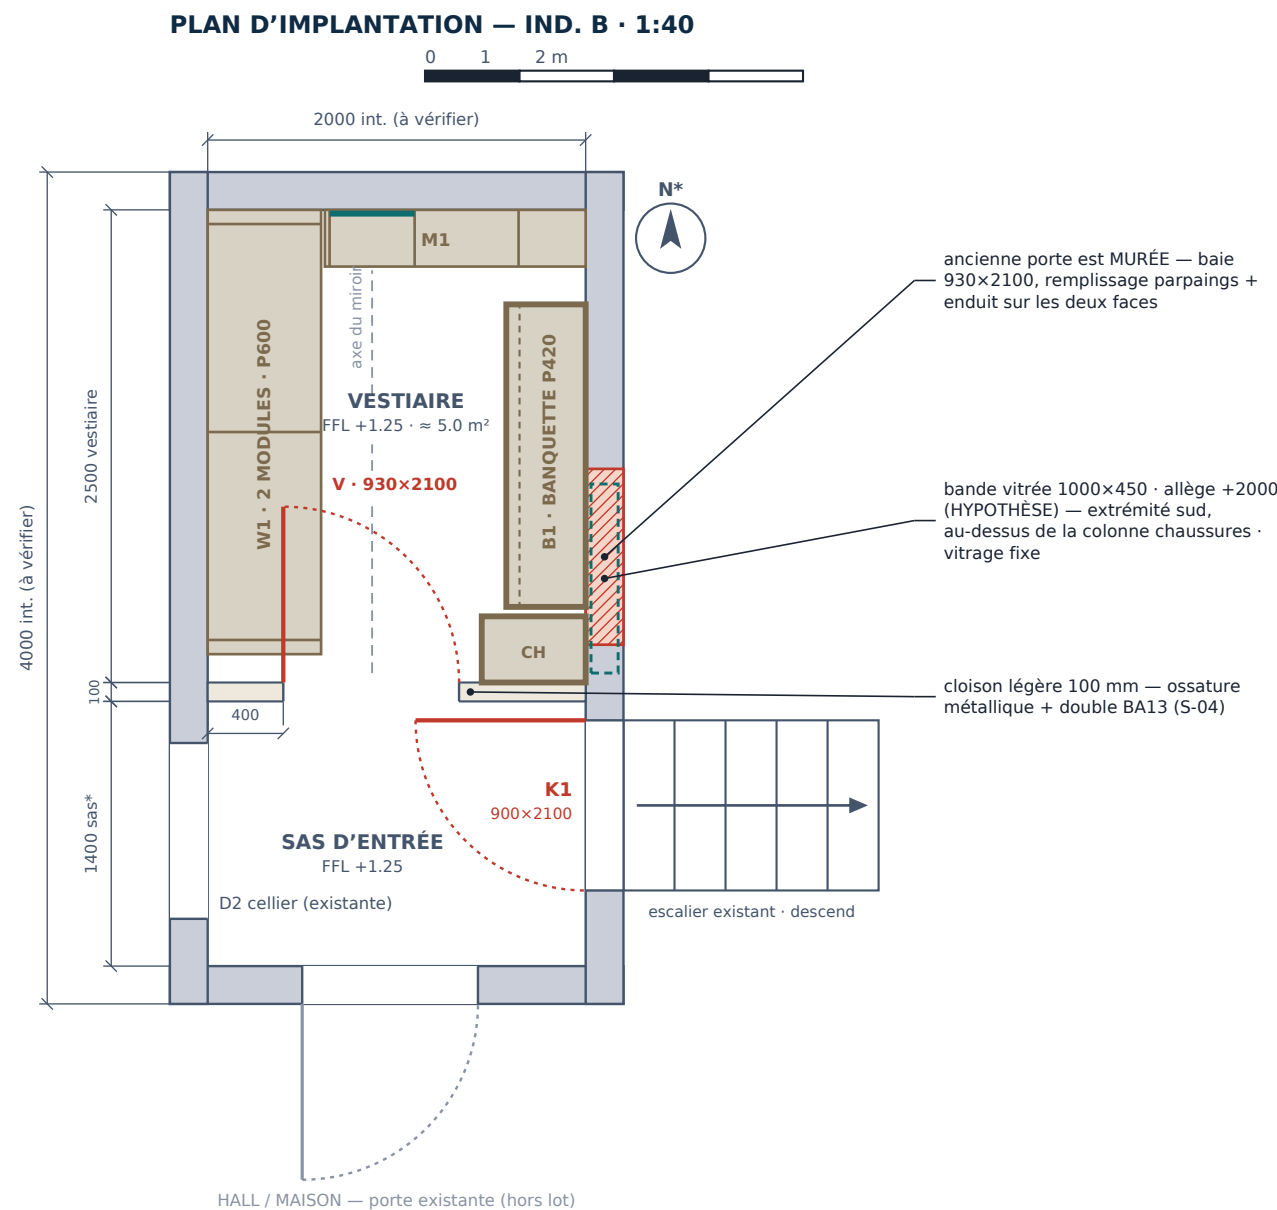




**NOTES S-01**

- Implantation Ind. B : SAS D'ENTRÉE (2000×1400*) + cloison légère (100) + VESTIAIRE (2000×2500). Les ouvrages murs/sols figurent dans le dossier principal ; le présent jeu définit l'agencement + la cloison + les débattements de portes.
- *Profondeur du sas 1400 mm : HYPOTHÈSE — à vérifier au relevé (illisible sur le plan) ; figée le jour du métré.
- Ancienne porte est (côté escalier) SUPPRIMÉE — baie murée ; le mur est est entièrement dévolu à la banquette B1.
- K1 : porte extérieure vitrée en aluminium à rupture de pont thermique 900×2100 · $U_w \leq 1.6$ · serrure RC2 · paumelles à fermeture automatique.
- V : porte intérieure bois 930×2100 ; à 400 mm du mur ouest — en entrant, on voit le miroir (M1) droit devant.
- Bande vitrée 1000×450, allège +2000 (HYPOTHÈSE — à vérifier au relevé) — extrémité SUD du mur est, zone au-dessus de la colonne chaussures ; vitrage fixe.
- Toutes les cotes en mm ; niveaux en mètres. Tapis de jute et petite quincaillerie mobile hors lot.

JUSTIFICATION DES SENS D'OUVERTURE (dimensions.json · swing_rationale)

- K1 ne doit pas s'ouvrir VERS L'EXTÉRIEUR au-dessus de l'escalier : cela pousserait la personne qui ouvre vers le vide de l'escalier et le vantail frapperait quiconque monte — risque de chute. K1 s'ouvre donc VERS L'INTÉRIEUR, sur le SAS ; les paumelles à fermeture automatique empêchent le claquement au vent.
- K1 est ferrée sur le montant nord : le vantail ouvert se range contre le mur nord du sas (la cloison) ; il ne gêne ni la porte de la maison ni le passage.
- Le sas étant étroit (1400), la porte V s'ouvre dans le VESTIAIRE, pas dans le sas ; ferrage sur le montant ouest — le vantail se range contre le panneau latéral de W1 et laisse libre l'axe d'entrée (porte → miroir).
- Même avec les deux portes ouvertes en même temps, les vantaux restent dans des volumes différents — aucun scénario de collision. La porte hall/maison existante est inchangée (hors lot).


LÉGENDE

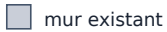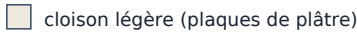- | | | |
|--|--|--|
|  mur existant |  ouvrages neufs / remplissage |  cloison légère (plaques de plâtre) |
|  agencement (présent lot) |  miroir / vitrage | |

CAD : output/CAD/S01_Yerlesim.dxf (Ind. B, mm 1:1) — même géométrie que la présente planche.

ORANGE — VESTIAIRE — PLANS DE FABRICATION (IND. B)

PLANCHE	ÉCHELLE	DATE	IND.
S-01 · Plan d'implantation (Ind. B)	1:40 @ A3	Juillet 2026	B
RELEVÉ SUR SITE OBLIGATOIRE AVANT TOUTE FABRICATION — ne pas fabriquer aux cotes du plan.			

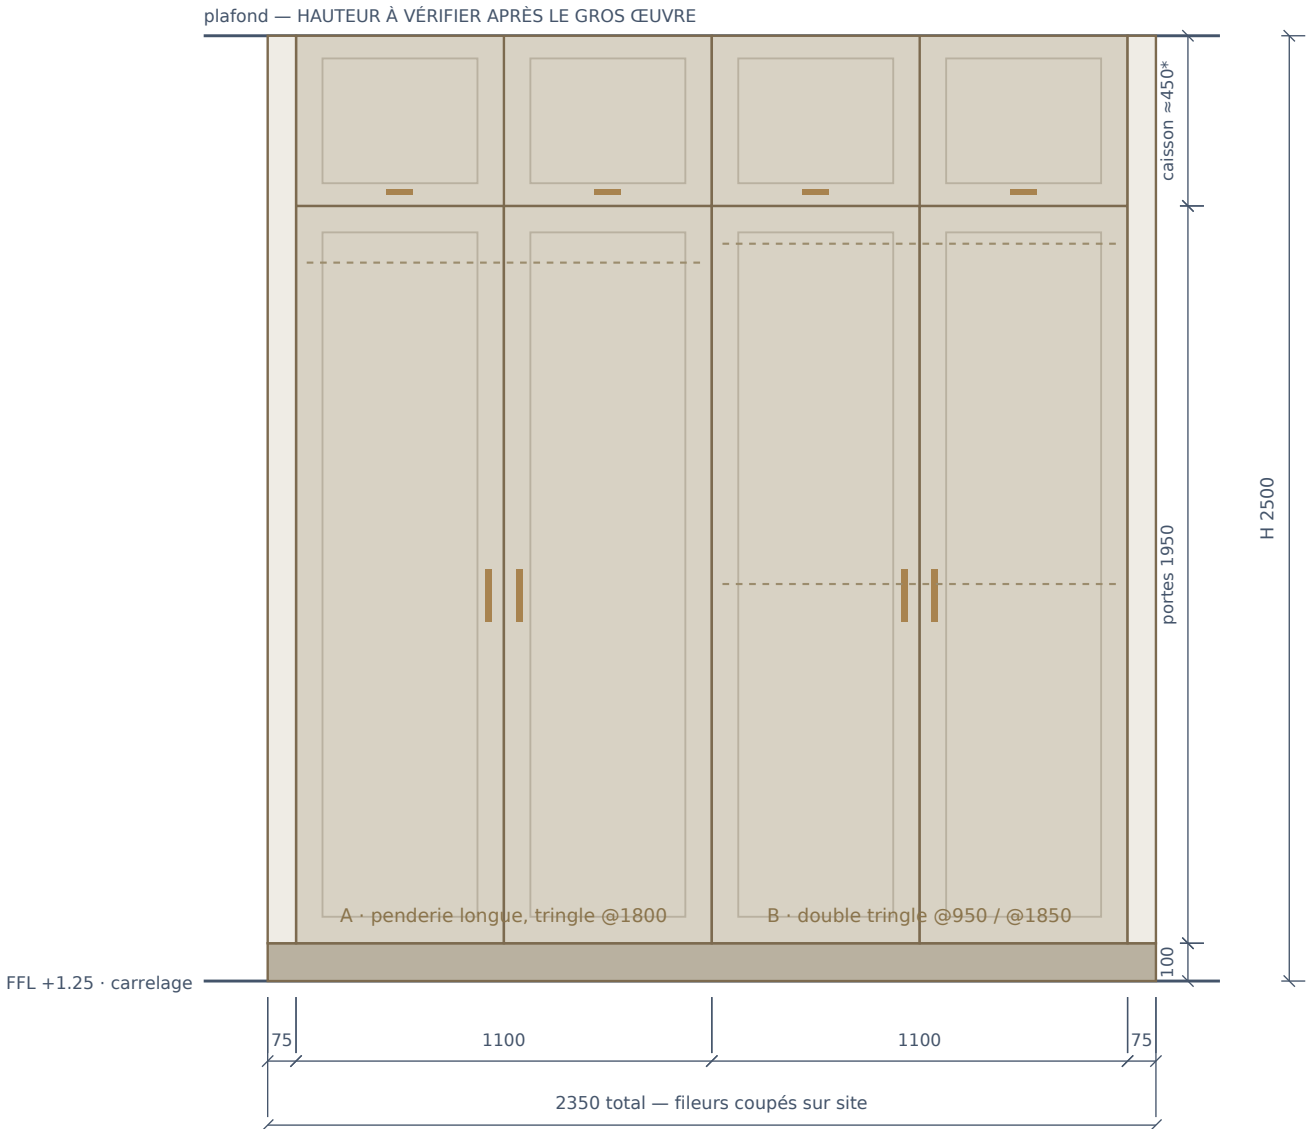

NOTES S-02


- Caissons en MDF hydrofuge 18 mm ; portes MDF 22 mm style shaker, laque PU greige ≈ RAL 7044 mat.
- *Les caissons hauts sont la zone de tolérance : si le plafond est plus bas, ils se raccourcissent — les portes 1950 restent invariables.
- Charnières : Blum Clip-top 110° à fermeture amortie — 3 par porte haute, 2 par porte de caisson haut (W1 : 20 pcs au total).
- Poignées : sur chaque porte ; verticales @1000 sur les portes hautes, horizontales près du chant bas sur les caissons hauts (W1 : 8 pcs).
- Aménagement : module A penderie longue (tringle @1800) · module B double tringle (@950 / @1850).
- Plinthe 100 mm sur vérins réglables ; plinthe clipsée, démontable.
- Fileurs de 75 mm nominal, aux deux extrémités — ajustés au mur sur site (tolérance ±15 mm).
- Le panneau latéral nord sert d'appui au meuble M1 (S-03) ; le vantail de la porte V se range contre le panneau latéral sud — ces faces reçoivent une laque anti-rayures, avec butée feutrée côté vantail.
- Traverses de fixation arrière chevillées dans le mur maçonné — jamais dans la seule plaque de plâtre.

CAD : output/CAD/S02_W1_Gorunus.dxf (Ind. B — 2 modules, mm 1:1).

ÉLÉVATION W1 (VUE VERS L'OUEST) · 1:20 — 2 modules à 2 portes de 1100 · portes 1950 + caissons hauts · caissons prof. 600


ORANGE — VESTIAIRE — PLANS DE FABRICATION (IND. B)

PLANCHE S-02 · Mur penderie W1 — Élévation (Ind. B)	ÉCHELLE 1:20 @ A3	DATE Juillet 2026	IND. B
RELEVÉ SUR SITE OBLIGATOIRE AVANT TOUTE FABRICATION — ne pas fabriquer aux cotes du plan.			

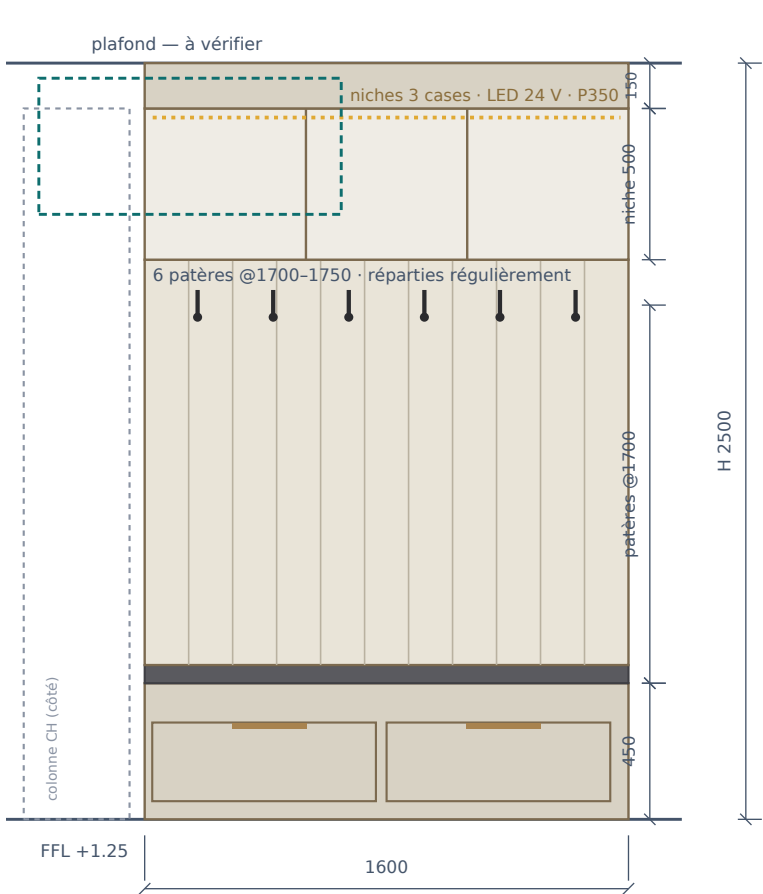


ÉLÉVATION B1 (VUE VERS L'EST) · 1:25

mur est — mur plein grâce à la baie murée ; 2 tiroirs Tandembox
bande vitrée 1000×450, allège +2000 (HYPOTHÈSE) — tirets : extrémité sud, au-dessus colonne CH

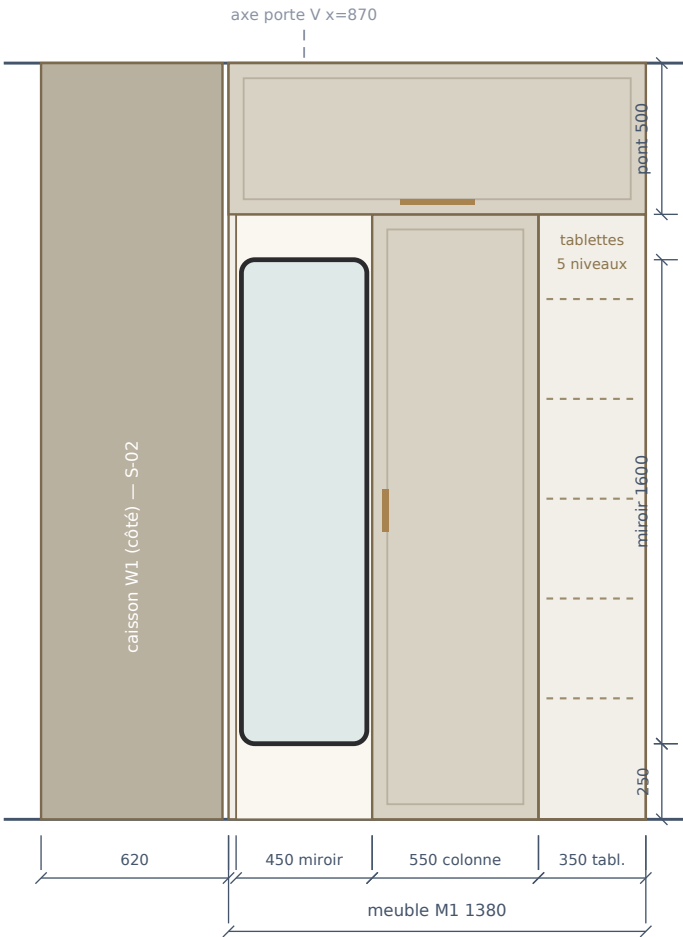

M1 MUR MIROIR — ÉLÉVATION MUR NORD · 1:25

miroir encastré sur l'axe de la porte V — vu droit devant en entrant ;
côté ouest = panneau latéral de W1

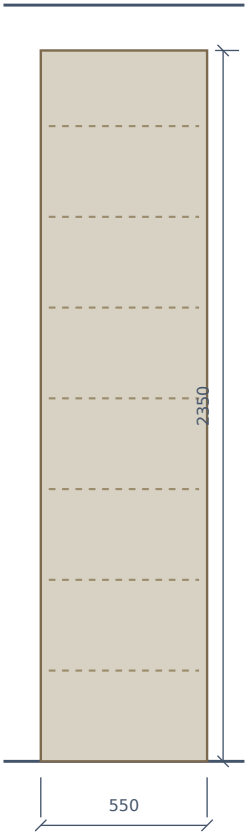

COLONNE CHAUSSURES · 1:25

550×350×2350 · 10 paires · vue vers le sud


NOTES S-03

- Caisson banquette 1600×450×420 ; coussin garni 60 mm sur l'assise (gris fumée) ; 2 tiroirs Blum Tandembox.
- Panneau porte-manteaux du dessus de banquette au-dessous de la niche ; 6 patères @1700-1750, noir mat.
- Bande de niches 1850-2350 : 3 cases, P350 ; LED 24 V 3000 K sous tablette (2.0 m au total), driver dans le bandeau haut.
- M1 : miroir encastré 450×1600 (bas à +250) sur l'axe de la porte V x=870 ; colonne à porte 550×2000 ; tablettes d'angle ouvertes 350, 5 niveaux ; pont haut 1380×500 (2000-2500).
- Le côté ouest de M1 s'appuie sur le panneau latéral nord du caisson W1 (ligne 620) — aucun panneau latéral supplémentaire.
- Colonne chaussures 550×350×2350 (10 paires) sur la face vestiaire de la cloison, extrémité est ; fixée à la cloison par une simple retenue anti-basculement.


CAD : output/CAD/S03_B1_Gorunus.dxf (Ind. B) —
même géométrie que la planche (mm 1:1).

ORANGE — VESTIAIRE — PLANS DE FABRICATION (IND. B)

PLANCHE S-03 · Banquette B1 + Miroir M1 + Colonne chaussures (Ind. B)	ÉCHELLE 1:25 @ A3	DATE Juillet 2026	IND. B
RELEVÉ SUR SITE OBLIGATOIRE AVANT TOUTE FABRICATION — ne pas fabriquer aux cotes du plan.			

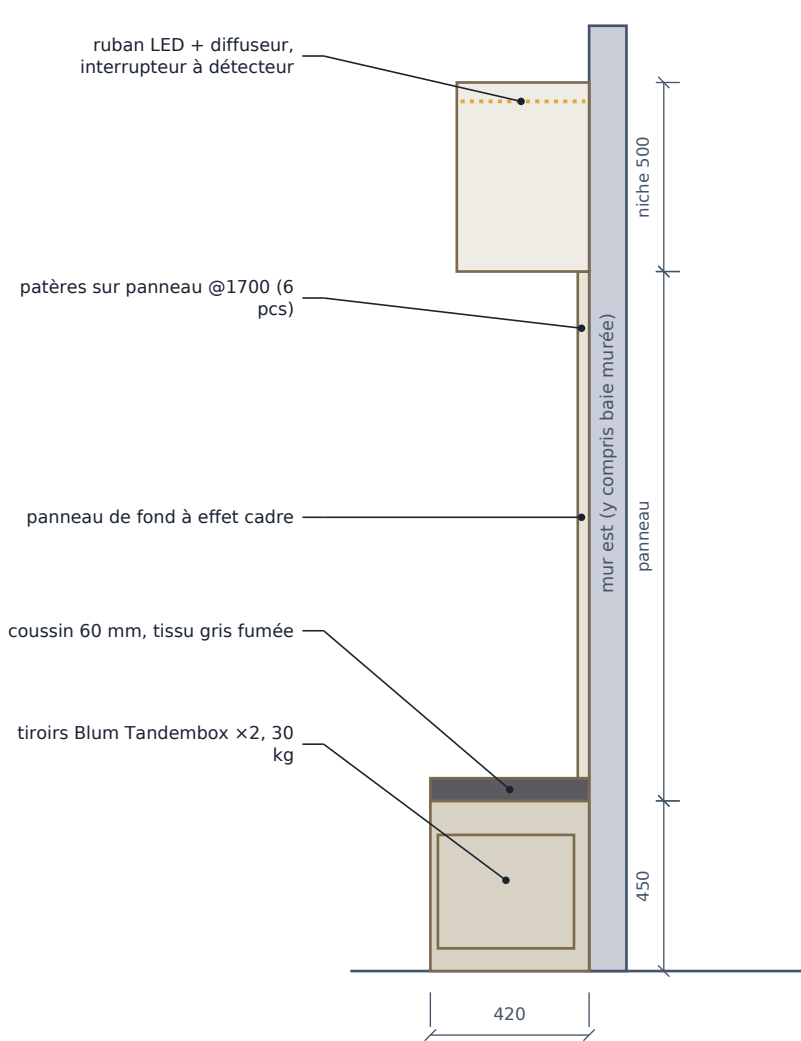

COUPE 1 — MUR BANQUETTE B1 · 1:20

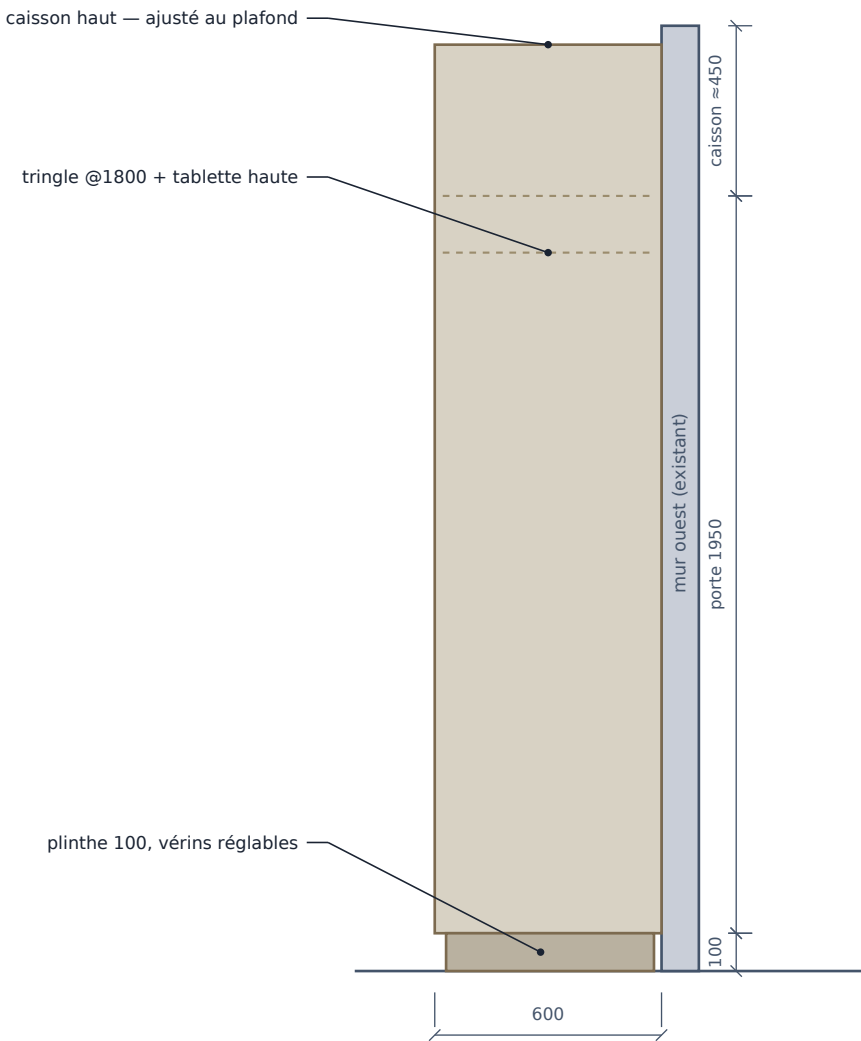


COUPE 2 — PENDERIE HAUTE W1 · 1:20

CAD : output/CAD/S04_Kesitler.dxf (Ind. B, mm 1:1) — détail de la cloison inclus.

NOTES S-04

- Coupes types ; les cotes de fabrication proviennent de la feuille de débit (révisée après le gros œuvre).
- Tous les chants vus laqués PU ; chants cachés plaqués de chant.
- Intérieur des niches en mélaminé couleur caisson ; profilé LED en retrait de 30 mm du nez de tablette.
- Cloison : montants métalliques DC50 entraxe 600, 2 plaques BA13 par face, laine minérale 45 mm (acoustique) ; volume chauffé des deux côtés — pas d’isolation thermique requise.
- L’hubriserie V se visse sur montants doublés dans la cloison ; rail haut en U en linteau au-dessus de l’hubriserie.
- Côté mur, panneau d’adossement 18 mm ; les vis d’ancrage traversent le panneau jusque dans le mur.

DÉTAIL — CLOISON SAS-VESTIAIRE (COUPE EN PLAN) · 1:5

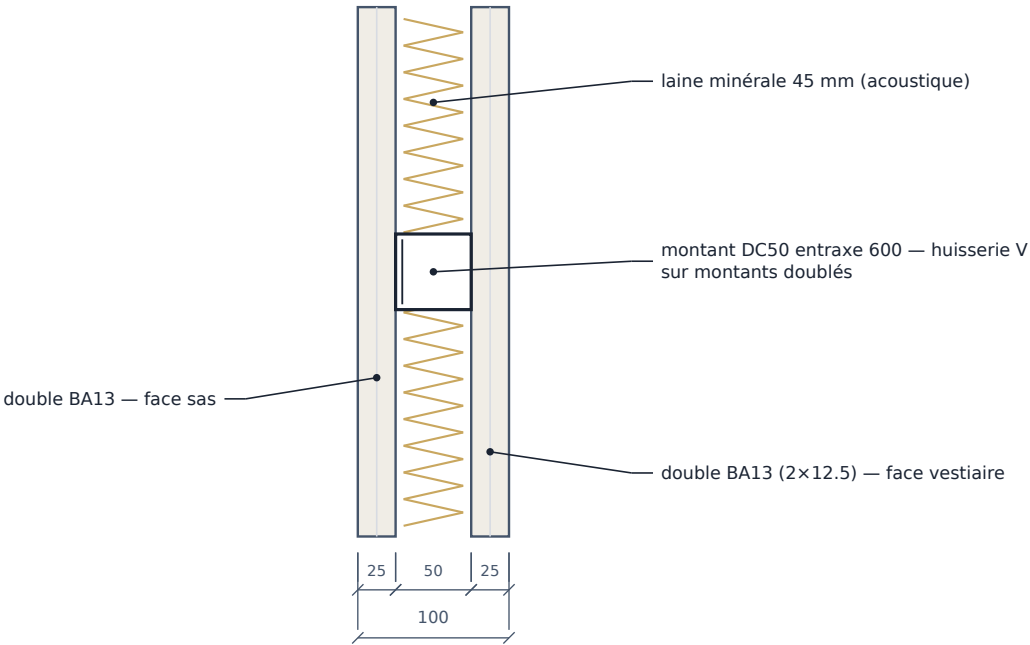

ORANGE — VESTIAIRE — PLANS DE FABRICATION (IND. B)

PLANCHE S-04 · Coupes — banquette, penderie, cloison (Ind. B)	ÉCHELLE 1:20 / 1:5 @ A3	DATE Juillet 2026	IND. B
RELEVÉ SUR SITE OBLIGATOIRE AVANT TOUTE FABRICATION — ne pas fabriquer aux cotes du plan.			

NOMENCLATURE QUINCAILLERIE ET MATÉRIAUX — QUANTITÉS IND. B

Composant	Spécification
Caissons	MDF hydrofuge 18 mm, chants plaqués ; fonds 8 mm en rainure
Portes et façades	MDF 22 mm style shaker, laque PU greige ≈ RAL 7044, mat
Charnières	Blum Clip-top 110° à fermeture amortie — 3 par porte haute, 2 par porte de caisson haut · W1 SEUL : 4 hautes × 3 + 4 caissons hauts × 2 = 20 pcs (charnières des portes colonne M1 et colonne chaussures dans leurs propres postes BoQ — non comptées ici)
Tiroirs	Blum Tandembox, sortie totale, fermeture amortie, 30 kg — banquette B1 : 2 jeux
Éclairage	Ruban LED 24 V 3000 K 2.0 m (bande de niches B1) + driver 1 + interrupteur à détecteur 1
Plinthe et vérins	Plinthe 100 mm, vérins réglables (14 pcs) ; clipsée, démontable
Fileurs	Fileurs de 75 mm (aux deux extrémités de W1), coupés sur site (≈ 5 ml)
Poignées	Laiton vieilli brossé ou noir mat, entraxe 128-160 mm — 10 pcs, W1+B1 SEULS (portes W1 8 + tiroirs B1 2 ; poignées colonne/pont M1 dans leur propre poste BoQ)
Patères	Patères doubles noir mat — 6 pcs, @1700-1750 (panneau B1)
Miroir	450 × 1600, cadre métallique noir, encastré dans la niche M1 — 1 pc
Cloison	Montants métalliques DC50 entraxe 600 + 2 BA13 par face + laine minérale 45 mm — 100 mm au total (S-04)
Assemblages	Tourillons + excentriques (CNC) ; ancrages muraux chevillés, ≥ 4 par caisson

RÈGLES DE FABRICATION

- La feuille de débit sera révisée d’après le relevé laser remis par le client à la fin du gros œuvre ; ne jamais lancer la fabrication aux cotes du plan.
- Les murs ne sont pas supposés d’aplomb : les fileurs portent une tolérance de ±15 mm ; l’agencement n’est jamais fabriqué au contact zéro des cotes nominales de maçonnerie.
- Tous les chants MDF coupés sont scellés (laque PU ou placage de chant) — pièce à chaussures mouillées.
- Panneaux numérotés par module (W1-A/B, B1, M1, colonne CH) ; le schéma de montage est conforme au PDF.
- Emballage : cornières de protection + intercalaires mousse + film anti-humidité + palette export ; limite ≈ 40 kg par panneau.
- Quincaillerie ensachée par module + 5 % de réserve ; pièces Blum dans leurs boîtes d’origine.
- Contrôle qualité : photos de chaque module envoyées au client avant emballage ; attendre son accord.
- Validation de la teinte : 1 porte échantillon + accord sur nuancier RAL obligatoires avant la série.

RÉFÉRENCES — IND. B

Source unique de vérité : data/dimensions.json (Ind. B, verified:false) · Contexte de conception : Orange_Mudroom_Conversion_Pack_A3.pdf · Dossier de consultation : lhale_Dosyasi_Vestiyer_TR.pdf (turc).
Quantités Ind. B (W1+B1 seuls) : 4 portes hautes + 4 caissons hauts + 2 tiroirs · 20 charnières (W1) · 10 poignées (W1 8 + B1 2) · 6 patères · LED 2.0 m · 14 vérins — colonne/pont M1 et colonne CH : quincaillerie dans leurs postes BoQ.
Anciens codes d’esquisse : D3 → K1 (porte extérieure du sas), D1 (porte est) → SUPPRIMÉE/murée ; V = porte du vestiaire (dans la cloison).

ORANGE — VESTIAIRE — PLANS DE FABRICATION (IND. B)

PLANCHE S-05 · Quincaillerie et matériaux + règles de fabrication (Ind. B)	ÉCHELLE — @ A3	DATE Juillet 2026	IND. B
RELEVÉ SUR SITE OBLIGATOIRE AVANT TOUTE FABRICATION — ne pas fabriquer aux cotes du plan.			