

Eşik Sayfası (K1 + V)


K1 dış eşiği: alçak, sızdırmaz, suyu atar · V iç geçişi: aynı kot, eşiksiz hedef

EK · K1 RÜZGARLIK KAPISI (ESKİ KOD D3)

Orange (84100) · Vaucluse · Fransa
Temmuz 2026 · Rev B · ana paketin ekidir

Kesit K1 (rüzgarlık kapısı) eşiği içindir: takılmadan geçilen alçak eşik, içeride kuru zemin, dışarıda suyu atan denizlik. V bir iç kapıdır: sahanlık ve vestiyer aynı kota (+1.25) yapıldığı için hedef EŞİKSİZ geçiştir — alttaki kurallara bakın.

K1 EŞİĞİ — KESİT ŞEMASI (ÖLÇEKSİZ, ORANLI)

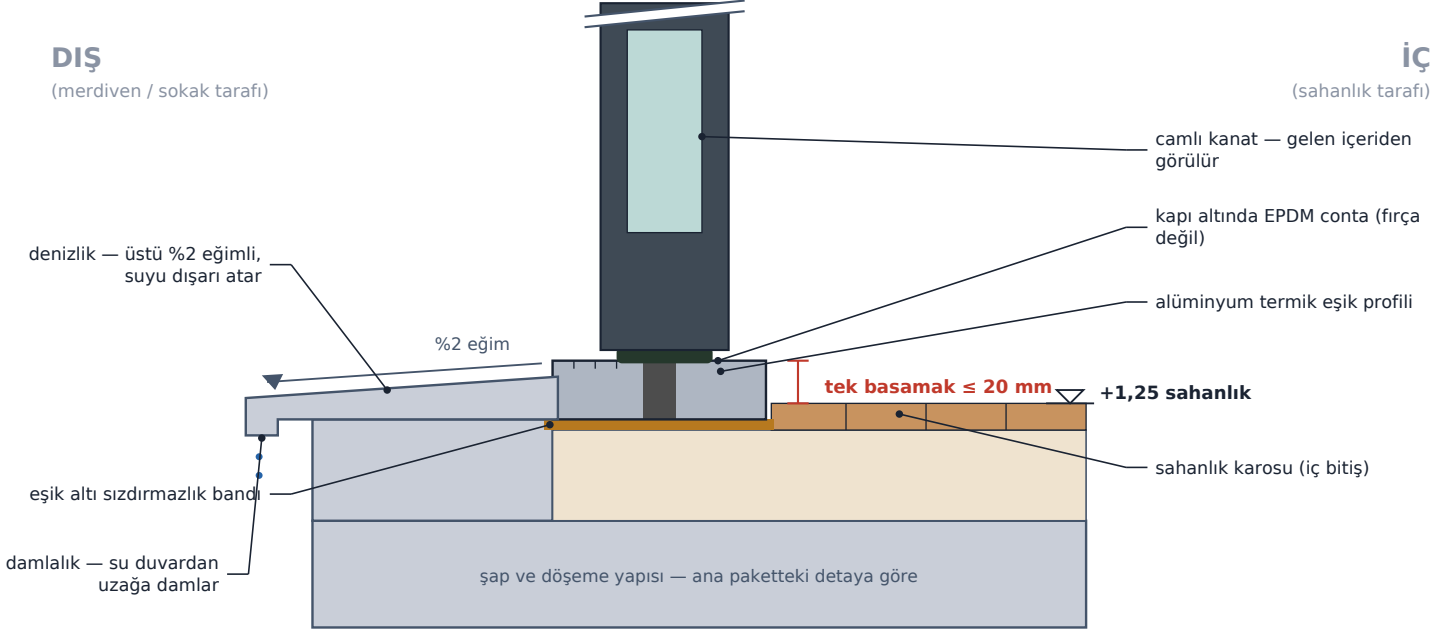

Şema ölçeksizdir; oranlar yaklaşıktır. İmalat öncesi yerinde ölçü zorunludur.

KURALLAR

- K1 önünde tek basamak en fazla 20 mm: daha yüksek eşik ayağa takılır ve erişilebilirliği bozar.
- Eşik altına sızdırmazlık bandı serilir; profil şapa değil, bandın üzerine oturur. Kapı altında fırça değil EPDM conta: hava ve suyu keser.
- Dış denizlik suyu dışarı atar: üstü %2 eğimlidir, damlalık kenarı duvar yüzünden dışarı taşar.
- V iç kapıdır: sahanlık ve vestiyer döşemeleri AYNI kota (+1.25) döküldüğü için eşik konmaz — hedef eşiksiz geçiştir; kapı altında yalnız kanat boşluğu kalır. Yerinde kot farkı çıkarsa ≤ 20 mm kuralı yine geçerlidir.
- Kotlar ve eşik ilişkisi yerinde ölçüyle kesinleşir — data/dimensions.json içindeki değerler verified:false durumundadır.

İKİ KAPI BİR BAKIŞTA

	K1 — rüzgarlık kapısı (eski kod D3)	V — vestiyer kapısı
Konum	Sahanlığın doğu kenarı, merdiven başı	Sahanlık kuzey duvarı (hafif bölme)
Nereye açılır	Sahanlığa, içe — menteşe kuzey	Vestiyere, içe — menteşe batı
Eşik	Bu sayfadaki detay — ≤ 20 mm	Eşiksiz — iki taraf aynı kot (+1.25) hedefi
Isı hedefi	$U_w \leq 1.6$ W/m ² K	$U_d \leq 1.4$ W/m ² K (iç kapı)
Kapsam	OPSİYON K1 — DP değişikliği onayı sonrası	Yerinde tedarik — ihale kapsamı dışı

Bu ek, ana paketteki çizim ve kuralların yerine geçmez; onlarla birlikte okunur.